


MicroStudio-PLC System Architecture Block Diagram

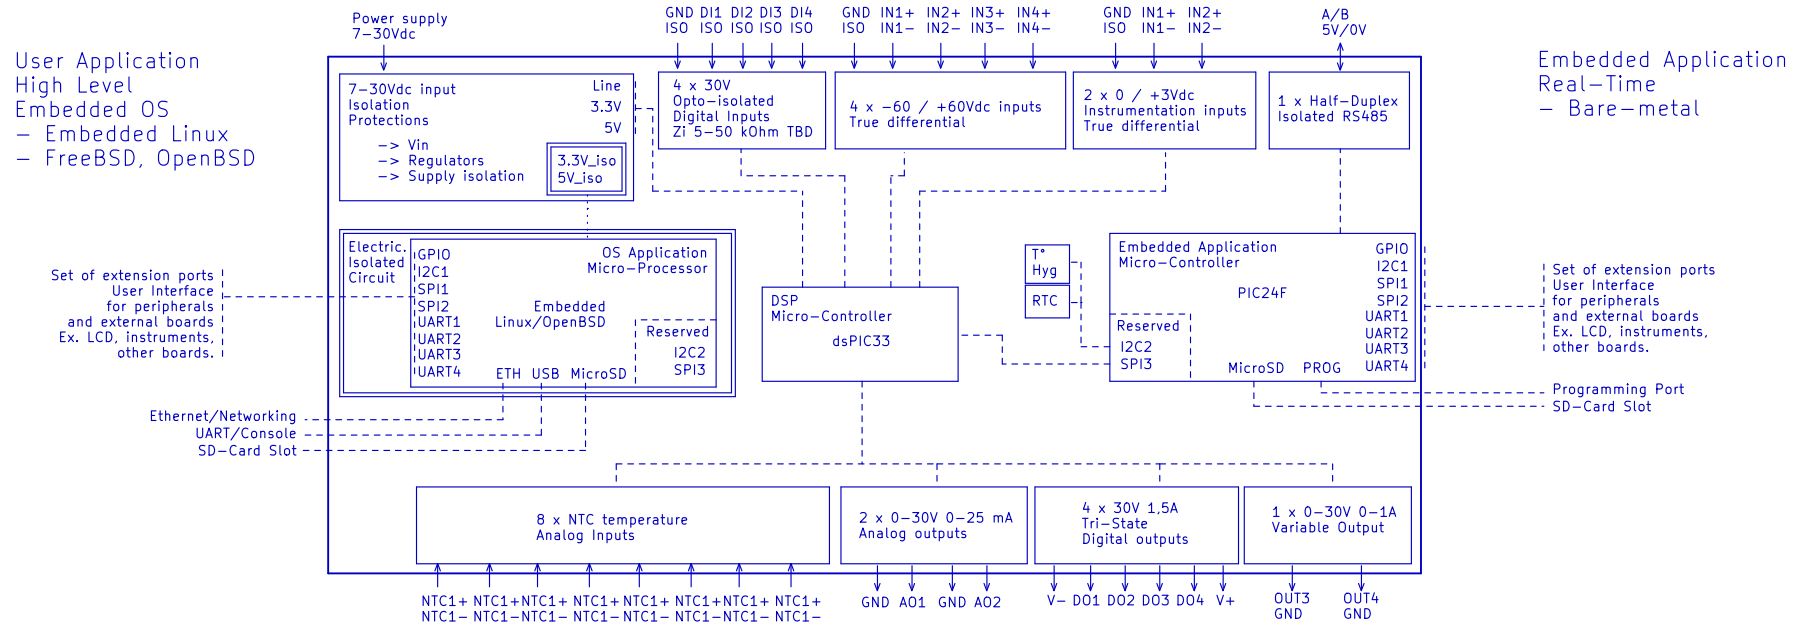

Chrysalide Lab
Measurements & Tests

Chrysalide Engineering SARL
141 rue du Lavoir
69870 Claveisolles, France
<https://chrysalide-engineering.com>
jfsimon@chrysalide-engineering.com

Sheet: /arch/
File: arch.kicad_sch

© Chrysalide Engineering - 2026.
Toute reproduction ou utilisation à des fins de brevet est interdite sans autorisation.

Title: MSPLC System Architecture

Size: A4 Date: 2026-06-24

Rev: 1.0

KiCad E.D.A. kicad (6.0.4)

Id: 2/3